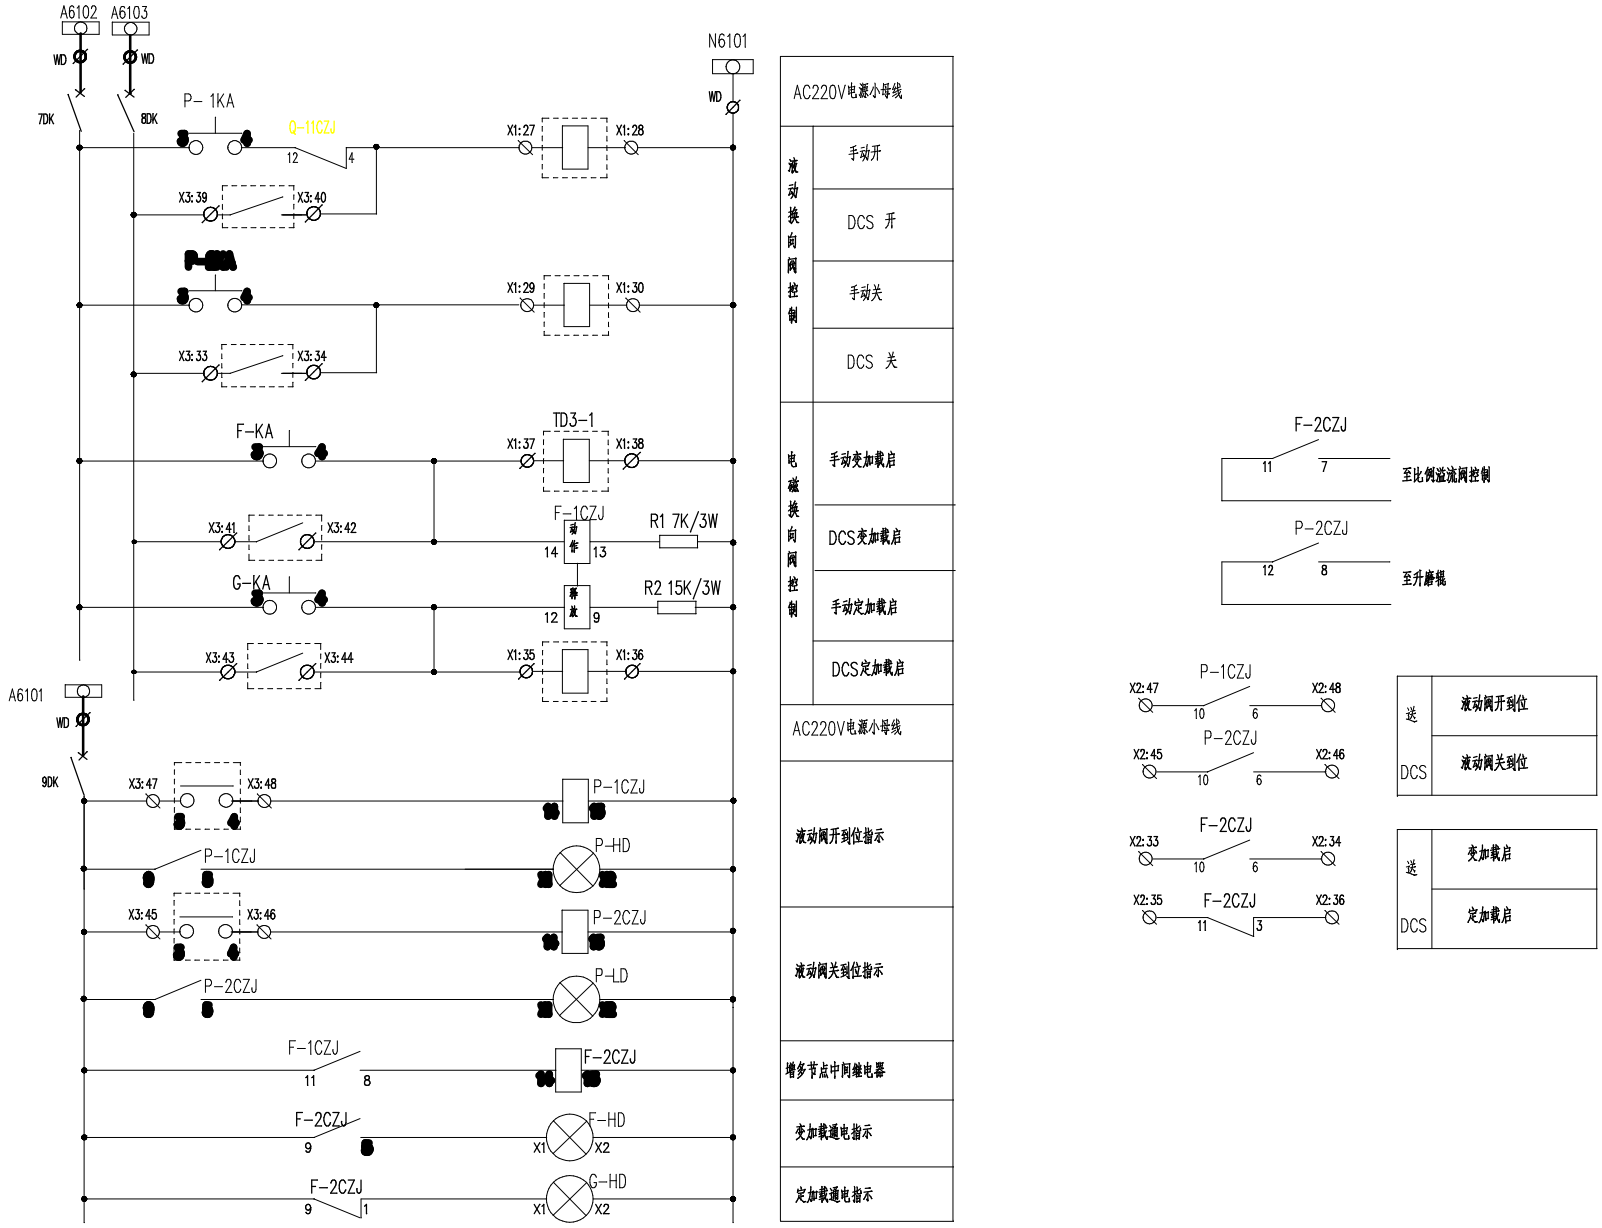


送DCS	
	液动阀开到位
	液动阀关到位

送DCS	
	变加载启
	定加载启

设计	刘雪伟	北京电力自动化设备厂	2020年2月技改图纸	图名	液动阀及定/变加载控制回路	图号	2020M02 MMJ.006.001