




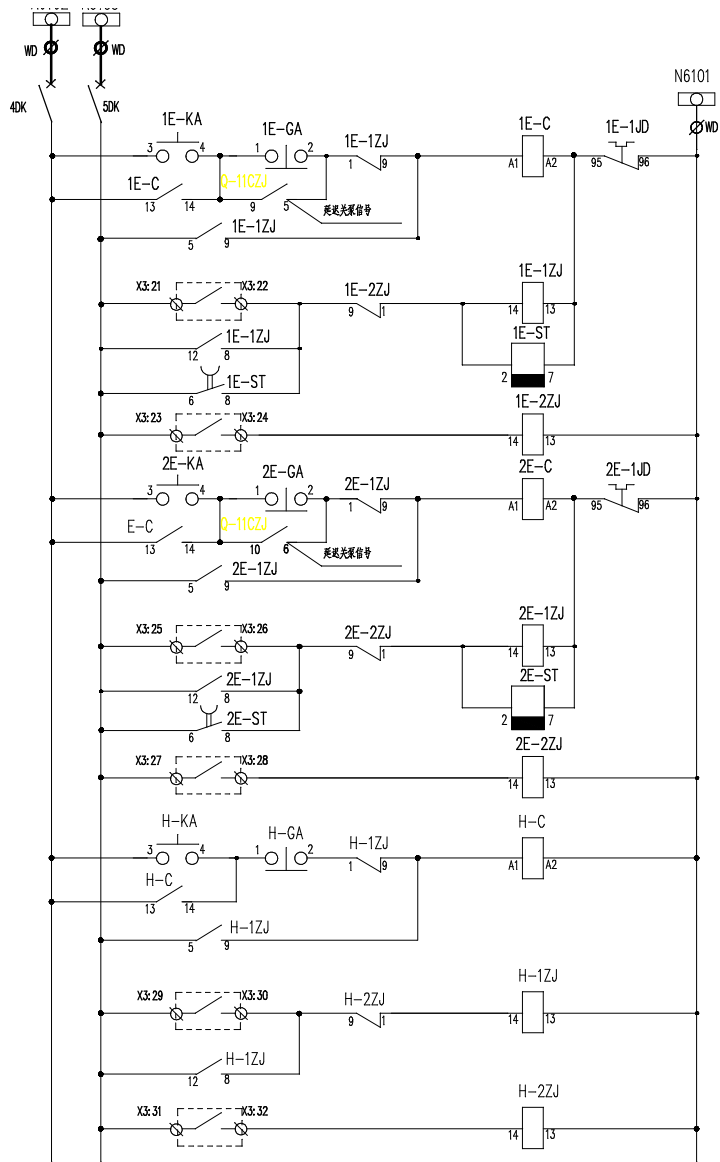

| AC220V电源小母线                                    |        |
|------------------------------------------------|--------|
| A<br>液<br>压<br>站<br>油<br>泵<br>控<br>制<br>回<br>路 | 手动启停   |
|                                                | 保持/扩接点 |
|                                                | DCS启动  |
| B<br>液<br>压<br>站<br>油<br>泵<br>控<br>制<br>回<br>路 | 手动启停   |
|                                                | 保持/扩接点 |
|                                                | DCS启动  |
| 电<br>加<br>热<br>器<br>控<br>制<br>回<br>路           | 手动启停   |
|                                                | 保持     |
|                                                | DCS启动  |

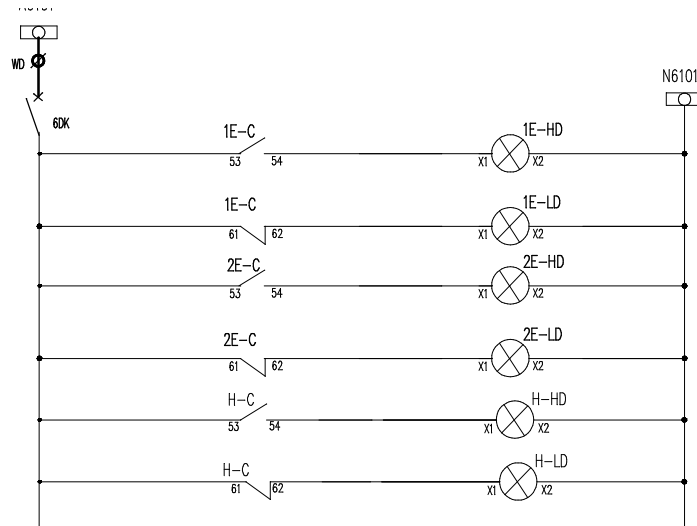

| AC220V电源小母线      |       |
|------------------|-------|
| A<br>油<br>泵      | 启(红灯) |
|                  | 停(绿灯) |
| B<br>油<br>泵      | 启(红灯) |
|                  | 停(绿灯) |
| 电<br>加<br>热<br>器 | 启(红灯) |
|                  | 停(绿灯) |

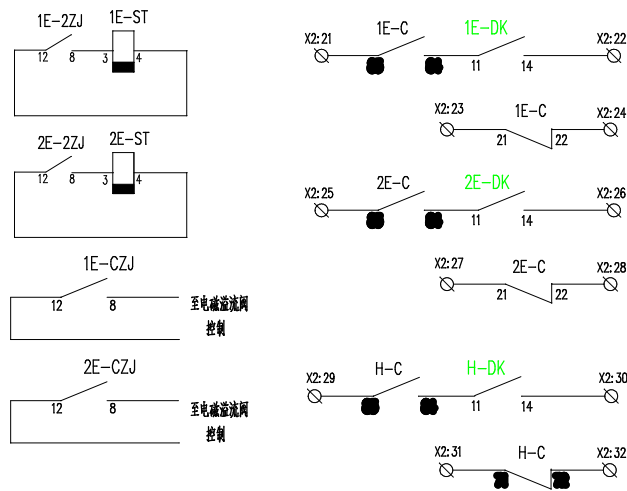

|                    |        |
|--------------------|--------|
| 至<br>DCS<br>信<br>号 | A加载油泵启 |
|                    | A加载油泵停 |
|                    | B加载油泵启 |
|                    | B加载油泵停 |
|                    | 电加热器启  |
|                    | 电加热器停  |

设计

刘雪伟

北京电力自动化设备厂

2020年2月技改图纸

图名

A/B加载油泵及电加热器控制回路

图号

2020M02

MMJ.005.001