
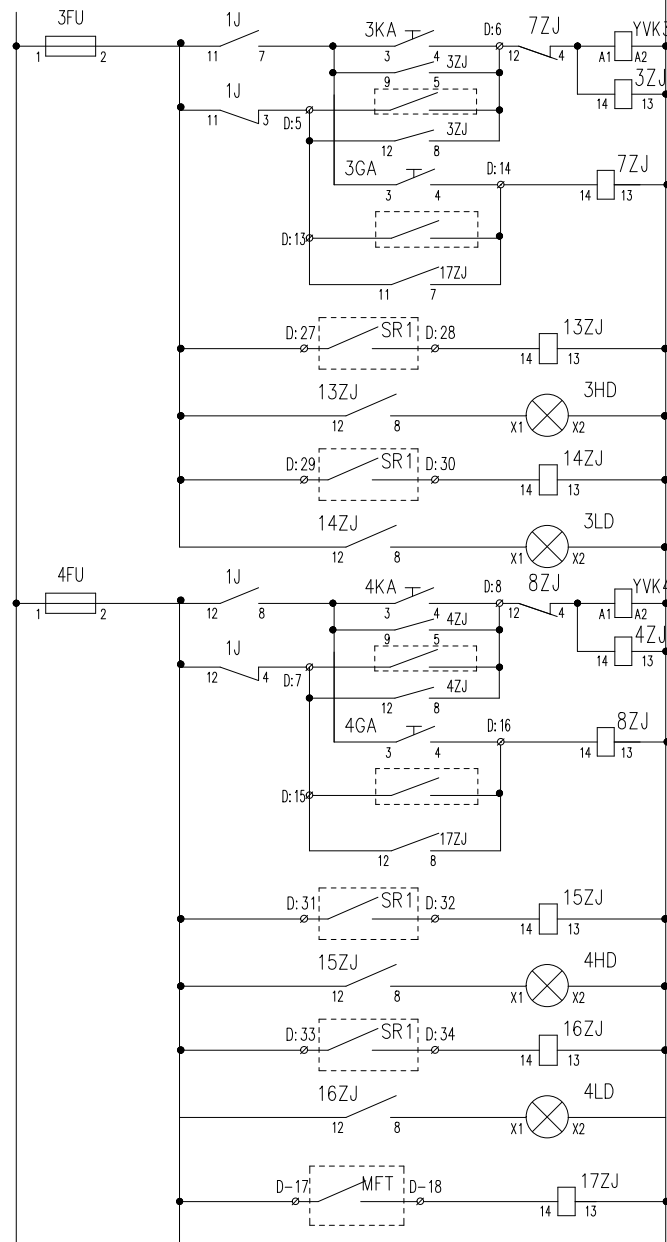


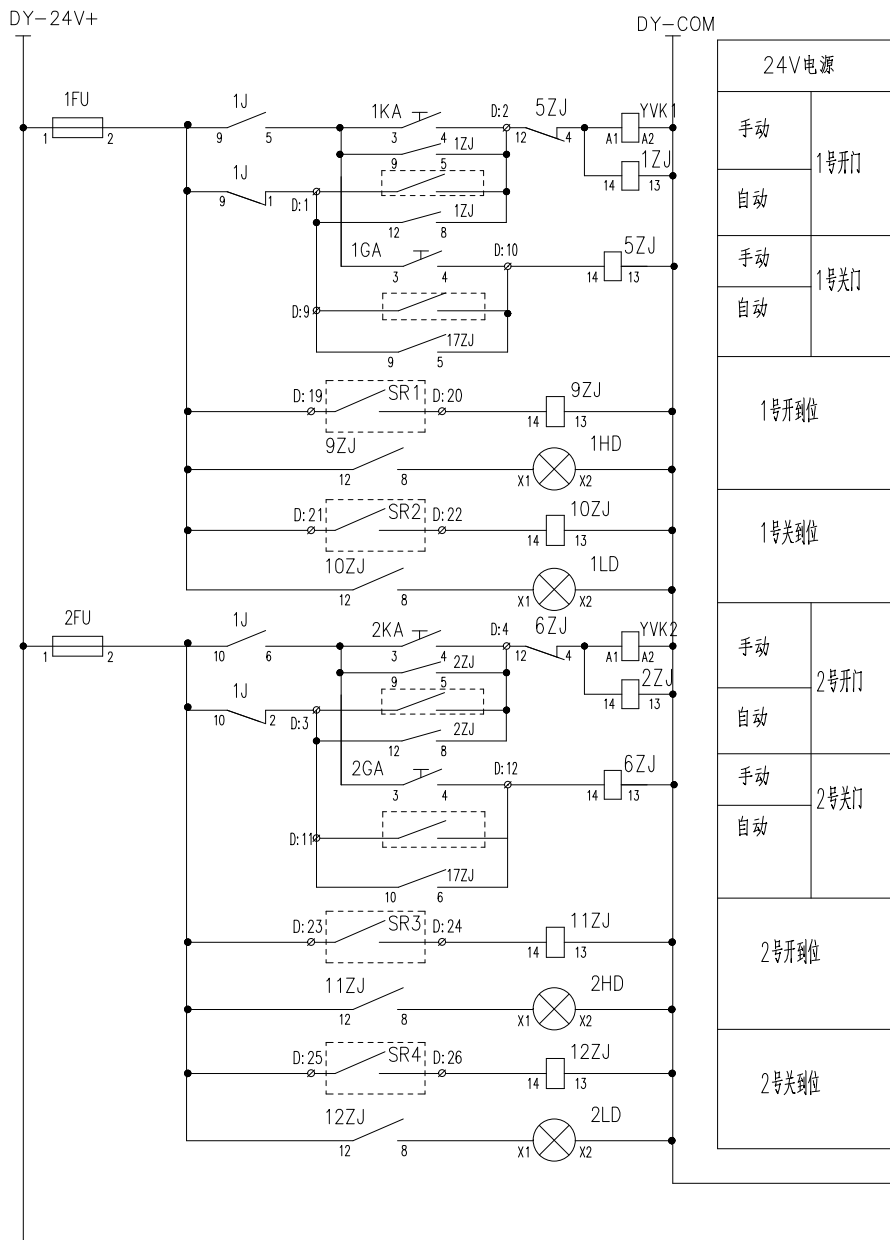

手动	3号开门
自动	3号关门
手动	3号关门
自动	3号关门
3号开到位	
3号关到位	
手动	4号开门
自动	4号关门
手动	4号关门
自动	4号关门
4号开到位	
4号关到位	
紧急关闭指令	

北京电力自动化设备厂

山西路安矿业(集团)有限责任公司高硫煤
清淤利用油、化、电、热一体化示范项目工程专用

图名

电气控制原理图1

档号

2014SX09

图号

SGM.002.000